

A

B

C

D

E

F

G

H

J

K

L

M


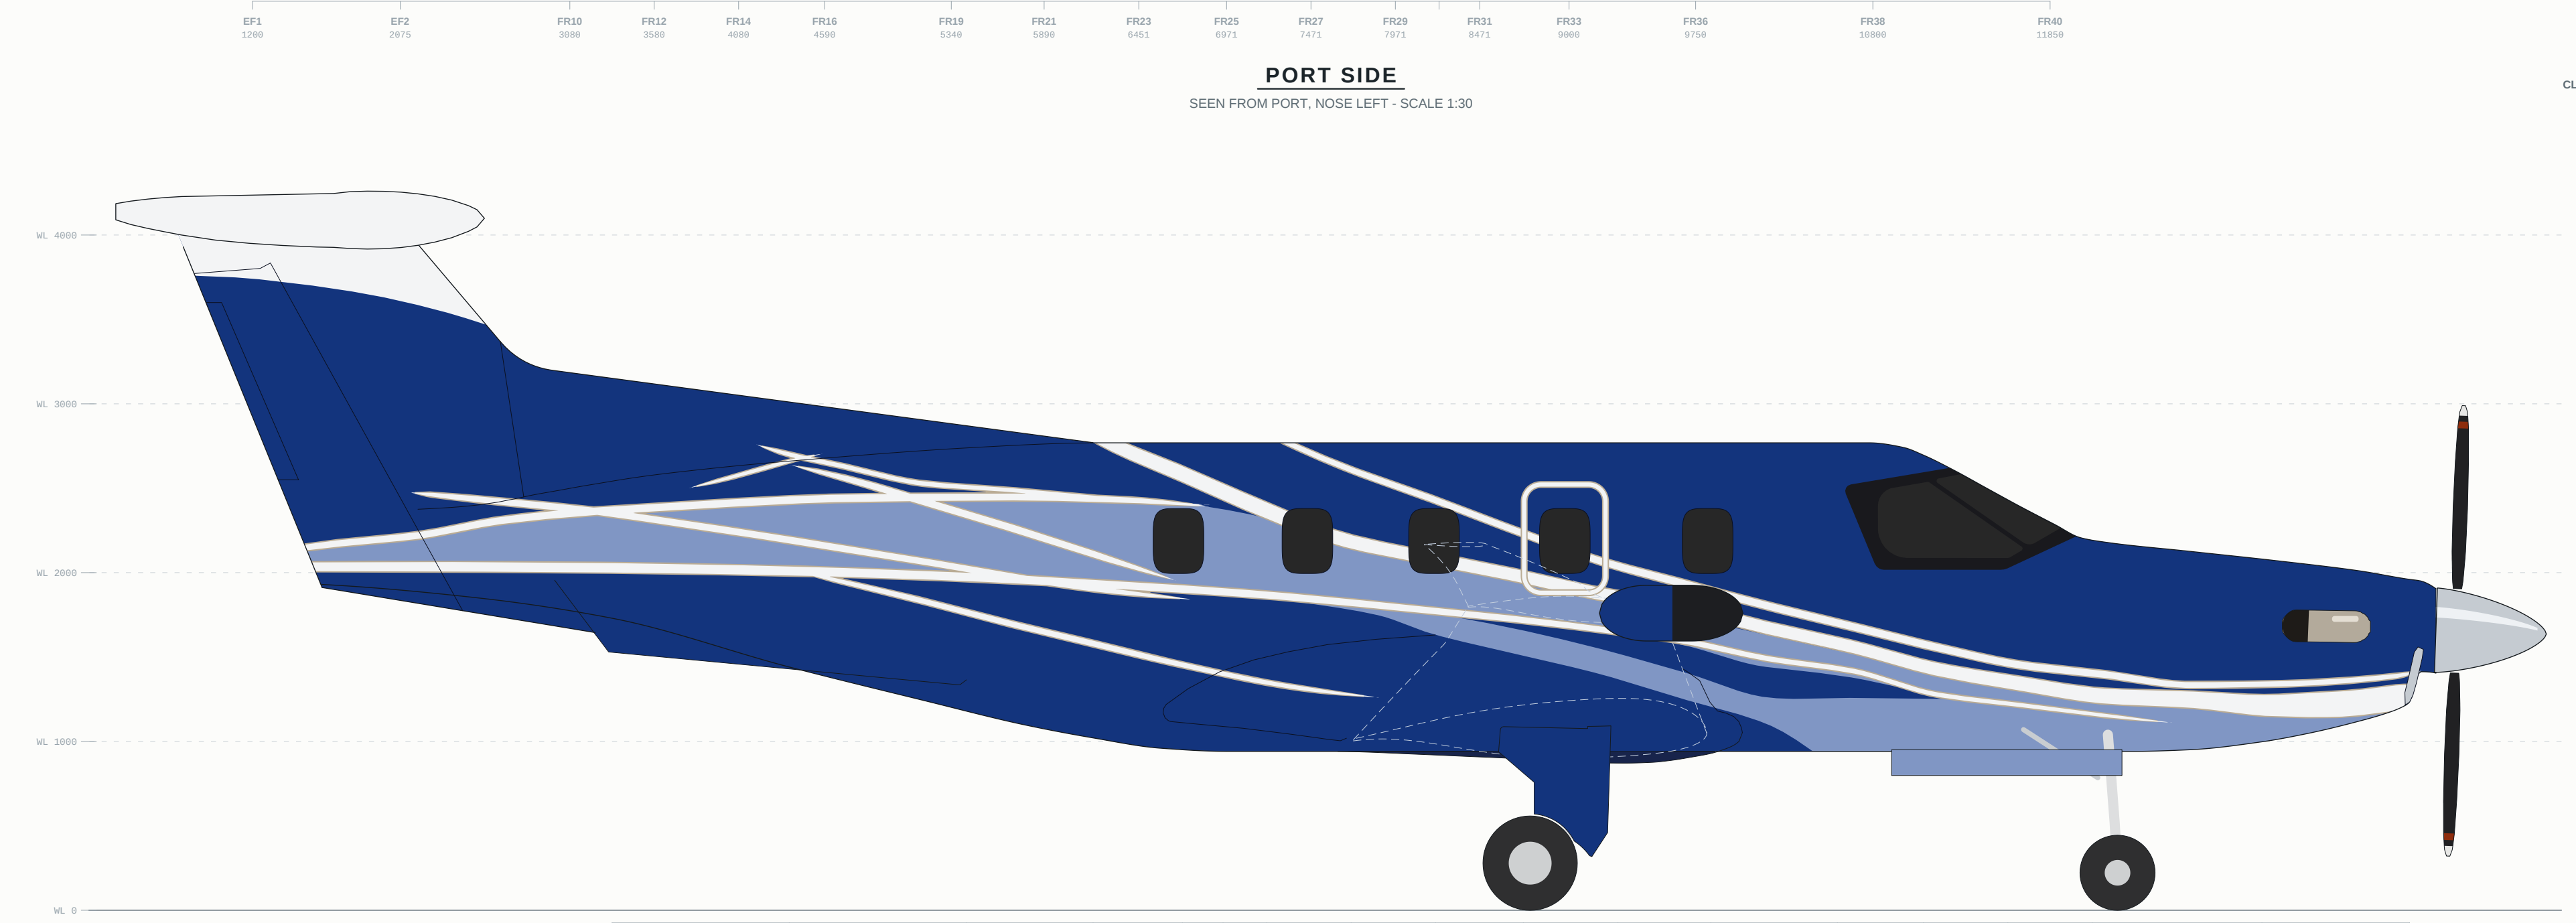


PHOTO SOURCES - MSN 3008 (N81DW), PILATUS NEWS 2025-09-26		
VIEW	PHOTO (refs/photos.json id; cand = refs/cache/photos/candipn_first-pc12-pro-hando-*)	USED FOR
starboard 3/4, ground	pro3008_sbd34_pilatus	camera-matched (13 points, 7 px rms), rectified onto the side projection: fuselage strokes, light band, fin cap, tailplane, leg door
starboard, air-to-air	cand_..._PC-12-PRO-N81DW	camera-matched (10 points, 5 px rms): tail-cone strokes, dark wing lower faces, white bullet, pod
port 3/4, hangar	pro3008_port34 (cand_130), cand_..._B2	camera-matched_130 (7 points, 8 px rms) and _B1 (7 points, 11 px): nose band group, light lower nose, blade bands, polished spinner / stacks
port nose, outdoors	cand_..._MSN-3008_188	B1 / P1 run parallel from the cowl front (base blue between them, no navy line: B2 / 130 too); champagne stroke edges
starboard wing, flight	cand_..._MG_0459	blue wing upper face, black LE boot, blue winglet with a white line, blue pod with a black radome

- NOTES
- Drawn from the parameters: every coloured area is the livery painter's field (model/livery.py) evaluated on the Stage-2 outlines (fuselage OML, glazing, openings, wing, empennage, gear, pod) - never from the mesh.
 - Fuselage / fin colours are side-projection curves: a surface point (x, y, z) takes the colour of (x, z), so strokes that reach the crown cross it (plan). Port = mirror of starboard (the photos show the same scheme).
 - Knots measured on the photos camera-matched to the model and rectified onto the side projection (+/- 0.03-0.05 m); the lower nose follows the port photos (the starboard nose is in shade).
 - Near wing drawn as phantom lines over the fuselage so the livery stays visible; propeller: 2 of 5 blades, schematic width; nose-gear doors open.
 - Estimated: plan-view crossings, winglet line position, lower-surface colours between photos, blade band widths (+/- 10 mm). No logos, lettering or registration marks are drawn.

DETAIL A - BLADE TIP

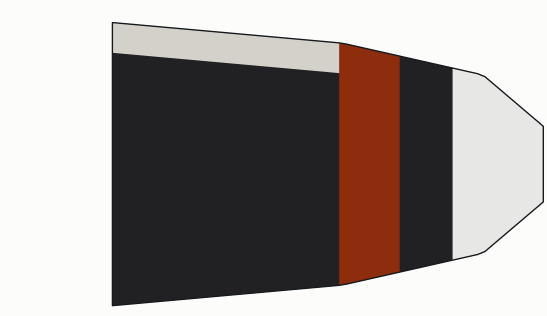

white tip / black / red band, measured inward from the tip (R 1335); leading edge (upper edge here); metal erosion strip 20 mm, R 400 to the red band

SCALE 1:30 (SIDE VIEWS, VIEW C)

SCALE 1:50 (PLAN)

PER-SURFACE COLOURS (model/livery.py SURFACES)			
livery SURFACES KEY		MATERIAL	WHERE
wing_upper / wing_lower	paint_blue	wing, flaps, ailerons, tabs: upper / lower face (normal light)	
winglet_inboard / outboard	paint_blue	winglet faces; WINGLET_FIN chordwise white line on the root blend	
stab_upper / stab_lower	paint_silver	tailplane + elevators; STAB_BOOT LE band (8 / 6 % chord)	
boot	paint_silver	wing ROOT_Y 0.05-1.43 and tailplane leading edges (black rubber)	
tailer / dorsal / strakes	paint_white	tailer fairing white; dorsal + strakes base blue	
body_fairing / flap_fairings	paint_wing_dark	dark wing paint	
pod_body / pod_radome	paint_blue	radar pod blue; radome black ahead of POD_X_JOINT	
main / nose_gear_door	paint_blue	leg doors blue; nose-gear doors light blue	
spinner / exhaust / blade_le	chrome	polished chrome / polished stacks / erosion strip	
inlet_lip / inlet_mouth	chrome	chin inlet (powerplant CHIN_INLET); polished lip ring, dark crescent mouth	



VIEW C - FRONT
SEEN FROM AHEAD, STARBOARD LEFT, WINGS BROKEN AT BL 2600 - SCALE 1:30

COLOUR LEGEND (model/livery.PALETTE -> model/assemble.MATERIALS)				
MATERIAL	USED FOR	sRGB	PBR LINEAR RGB	M / R
 paint_blue	base: fuselage, dorsal, fin, rudder, wing upper faces, winglet inboard faces, pod, leg doors	#1947D	0.007 0.034 0.205	0.30 / 0.50
 paint_blue_light	lower coating / lower nose, switch band to the lower rudder, nose-gear doors	#609C4	0.215 0.305 0.550	0.50 / 0.30
 paint_primer	primaries and secondarys (B1 P1 P2 P3 L1 L2 L3 L2628 L2			