

A

B

C

D

E

F

G



H

J


K

L

M

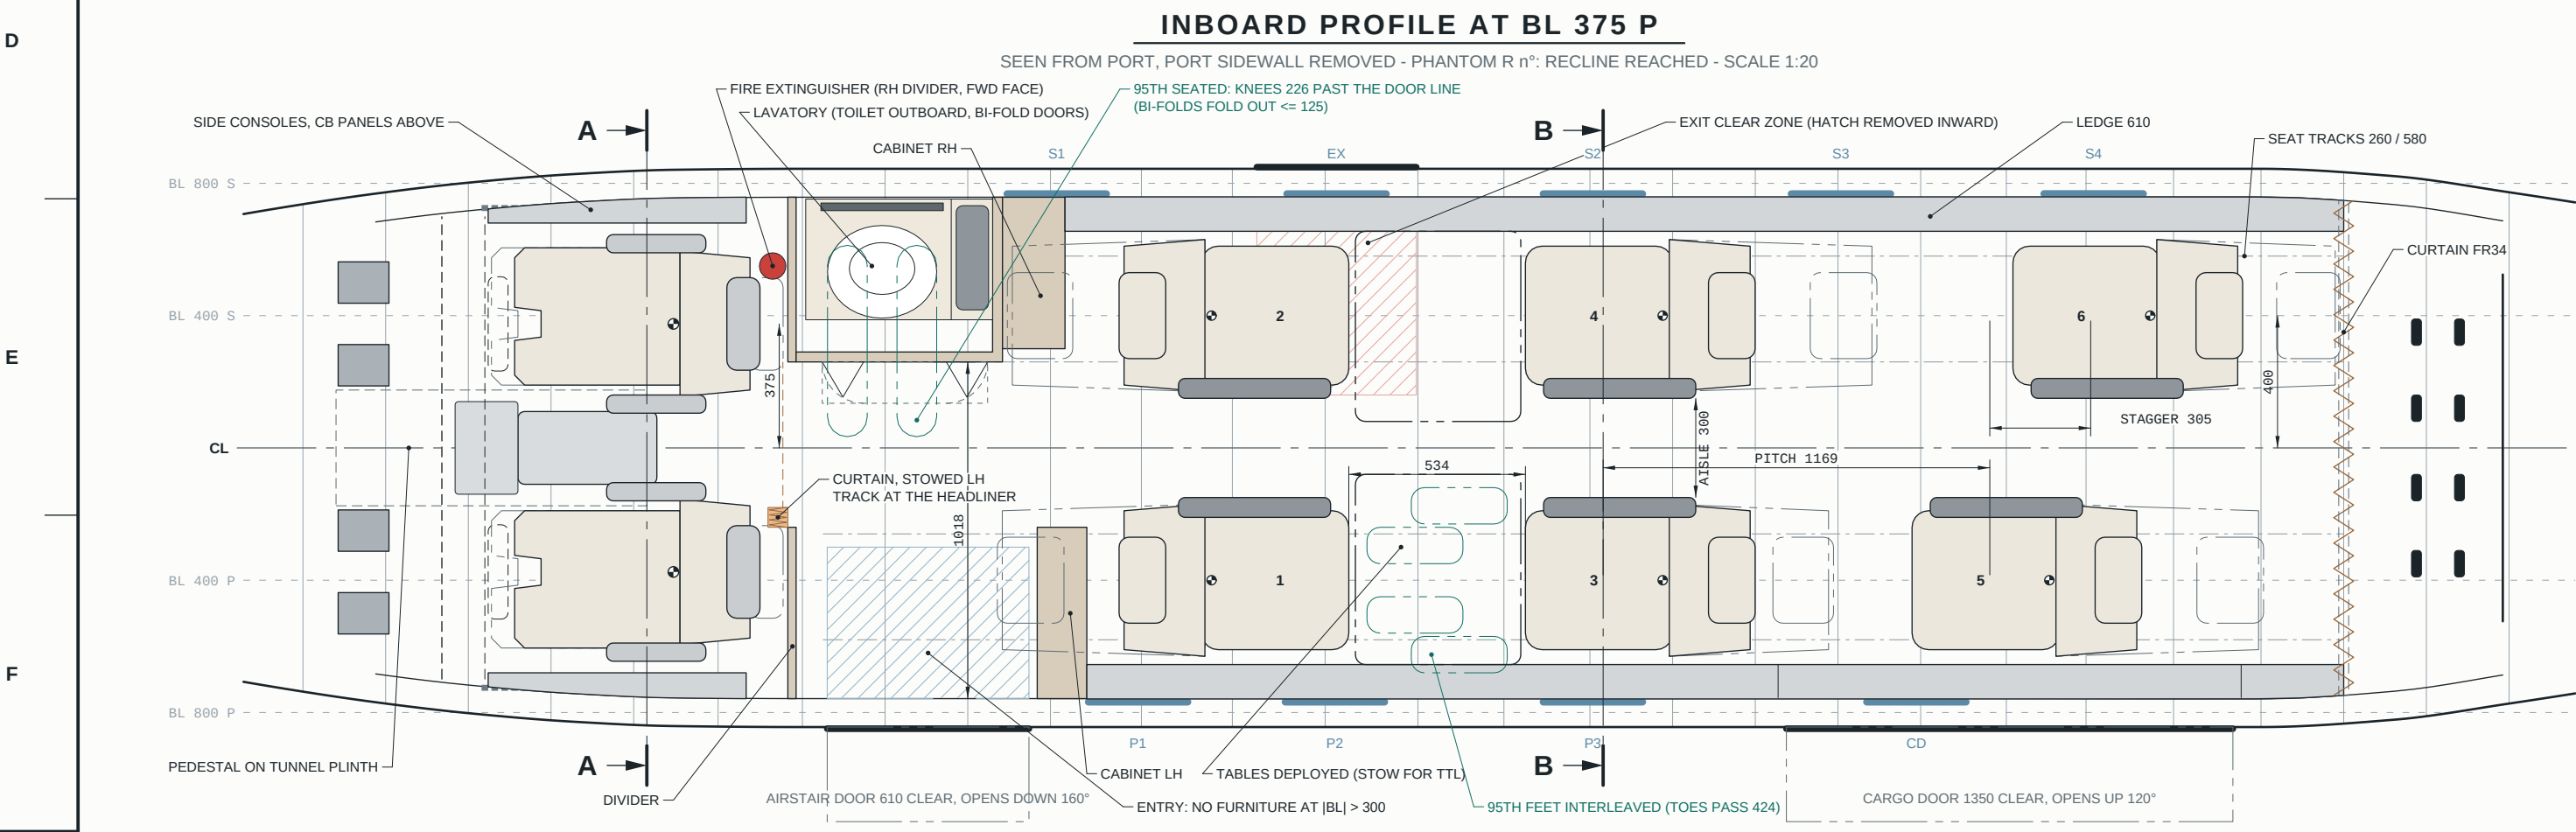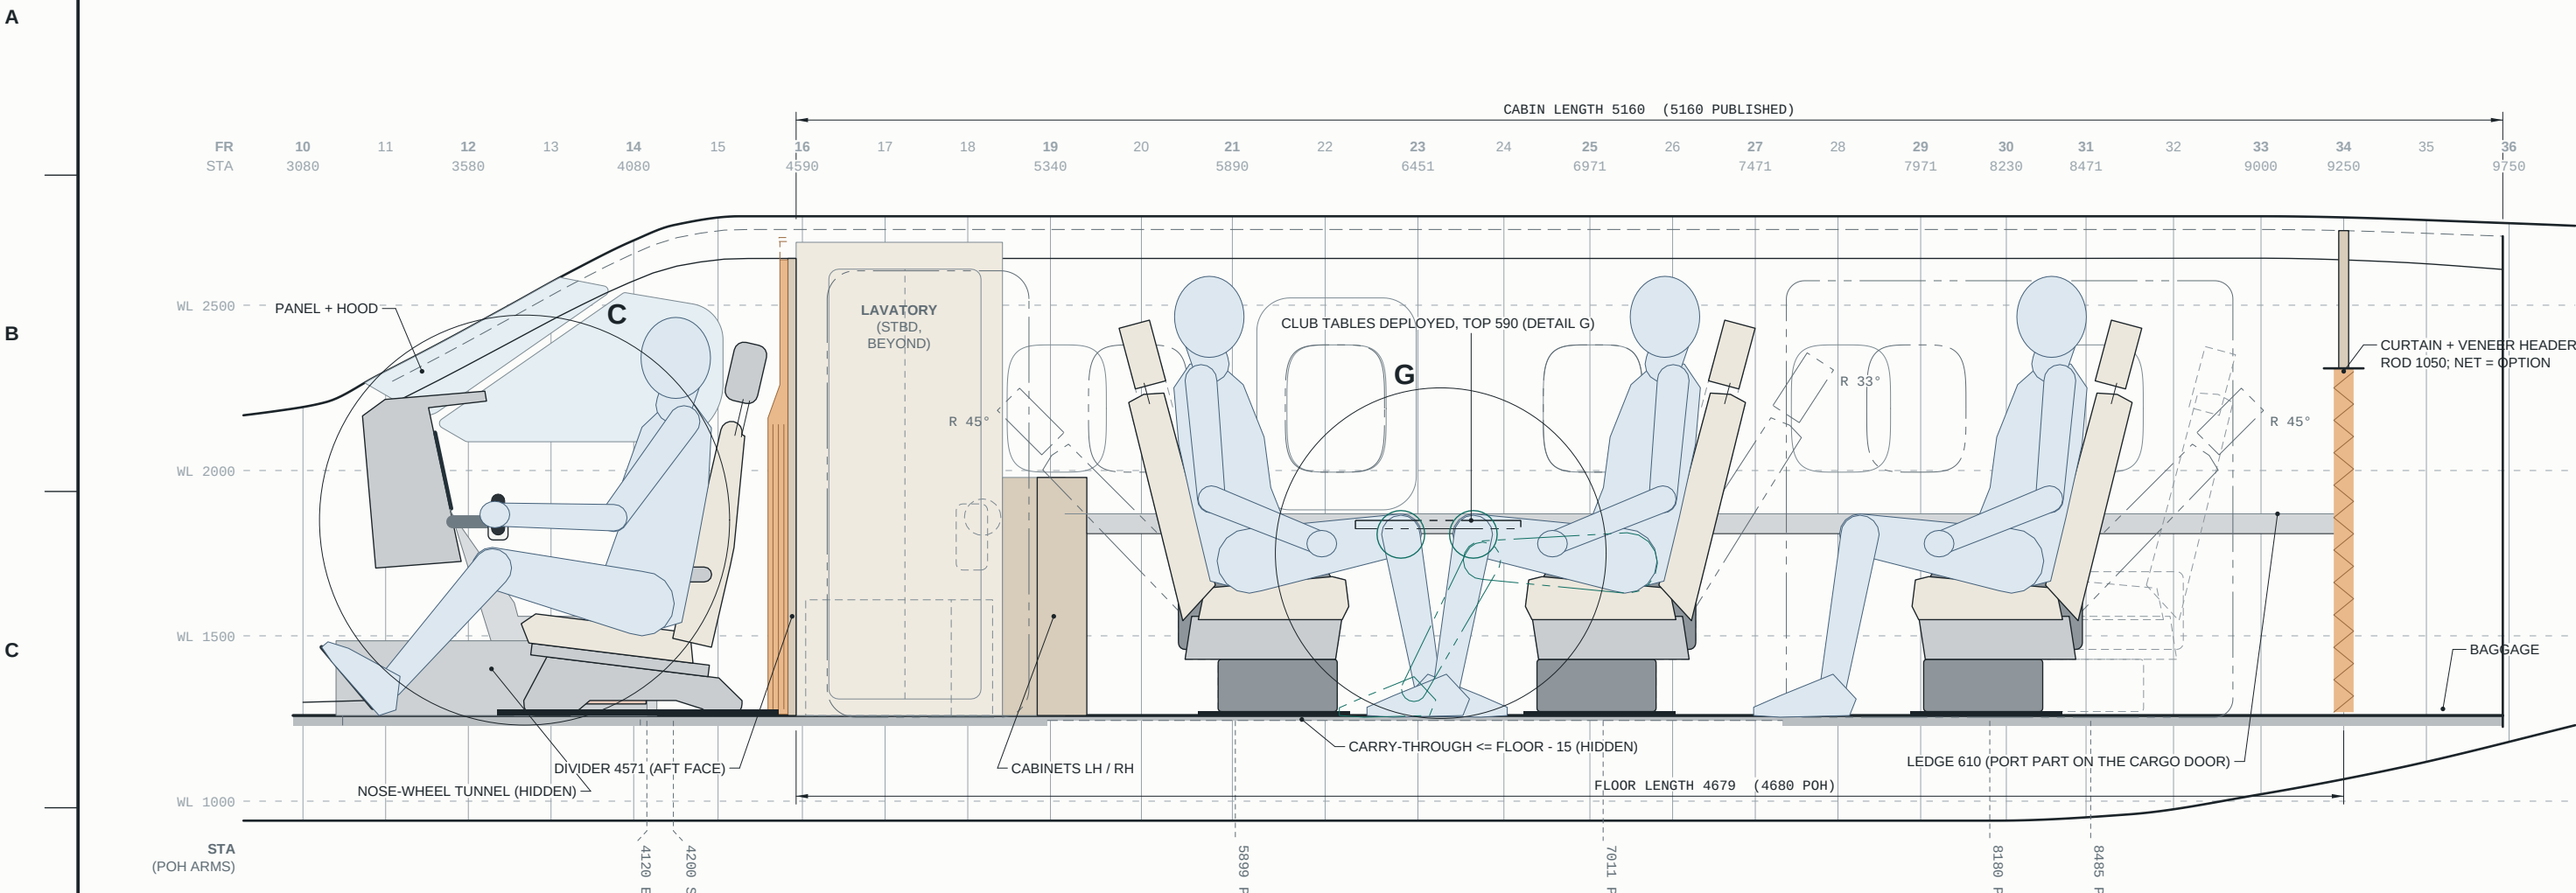


SECTION A-A
STA 4120, LOOKING AFT (STBD LEFT) - SCALE 1:10
PHANTOM: KNEES, LEGS, HANDS FORWARD OF THE CUT

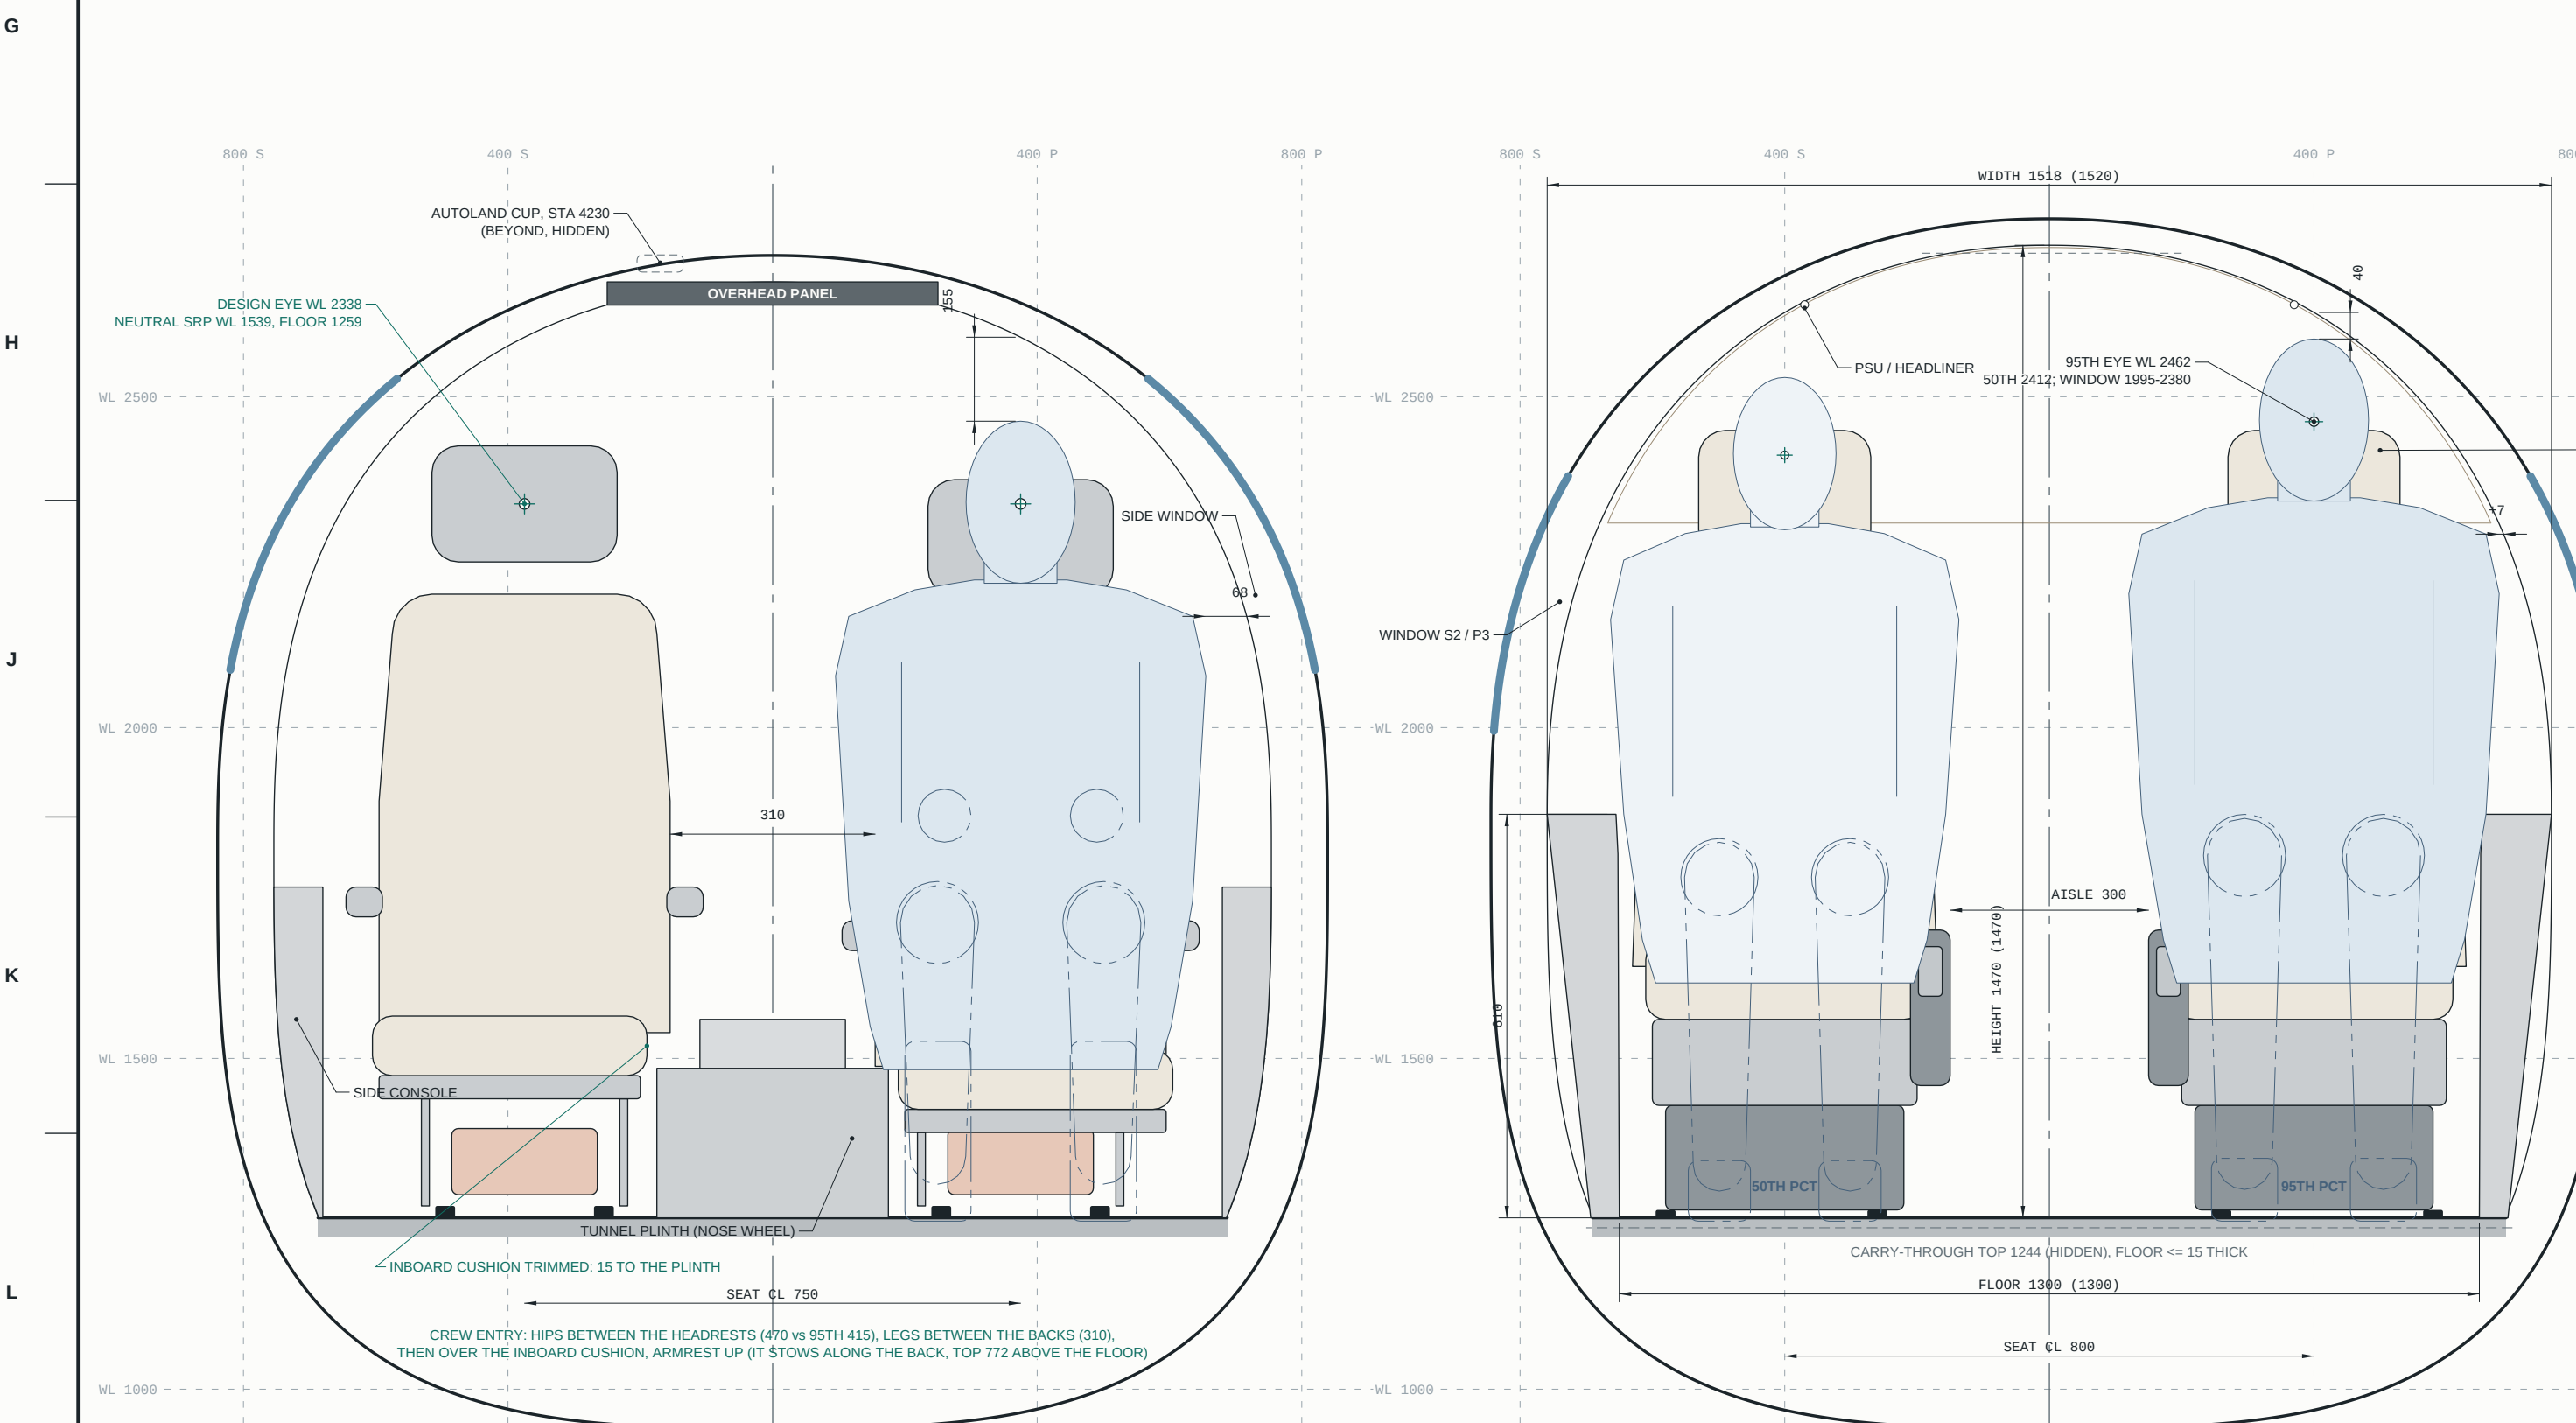


SECTION B-B
STA 7011, LOOKING AFT (STBD LEFT) - SCALE 1:10
PHANTOM: KNEES, LEGS FORWARD OF THE CUT - BROWN: FR34 HEADER + ROD, BEYOND


M

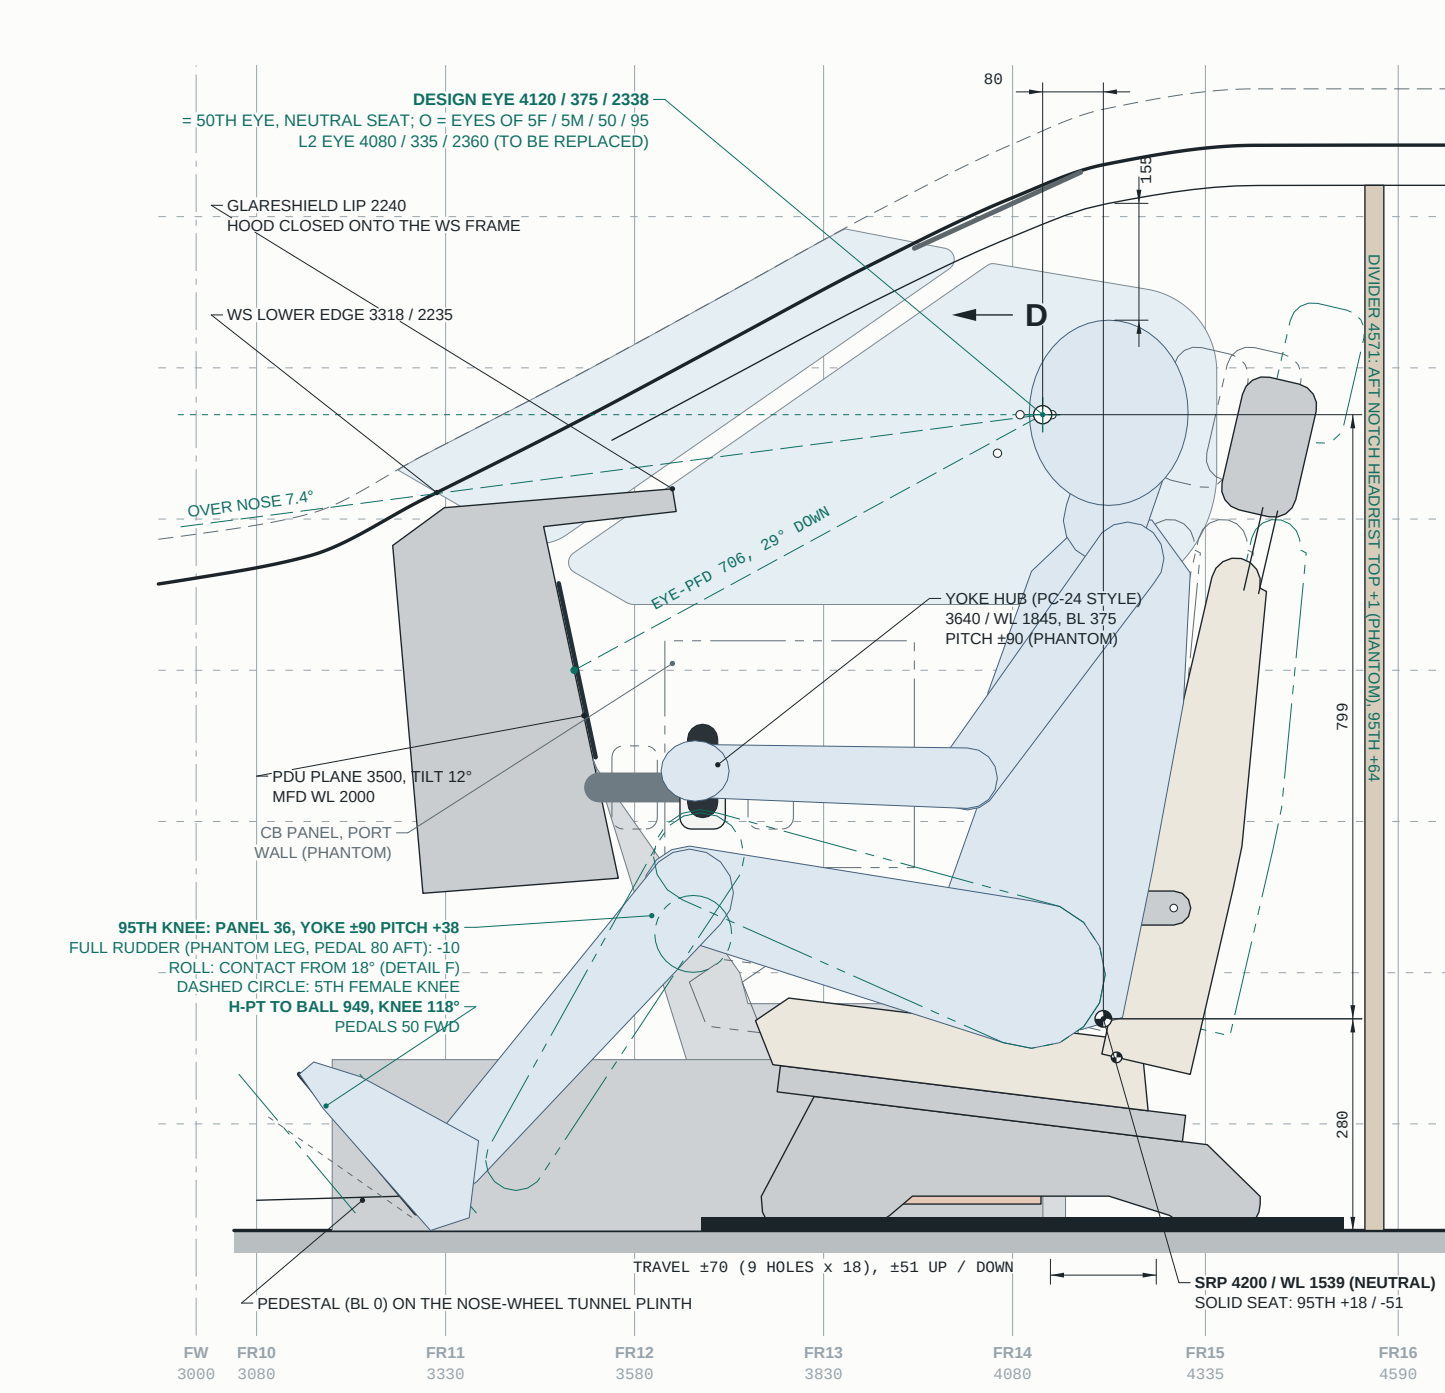

DETAIL C - CREW STATION
LEFT SEAT, BL 375 P, SEEN FROM PORT - SCALE 1:10

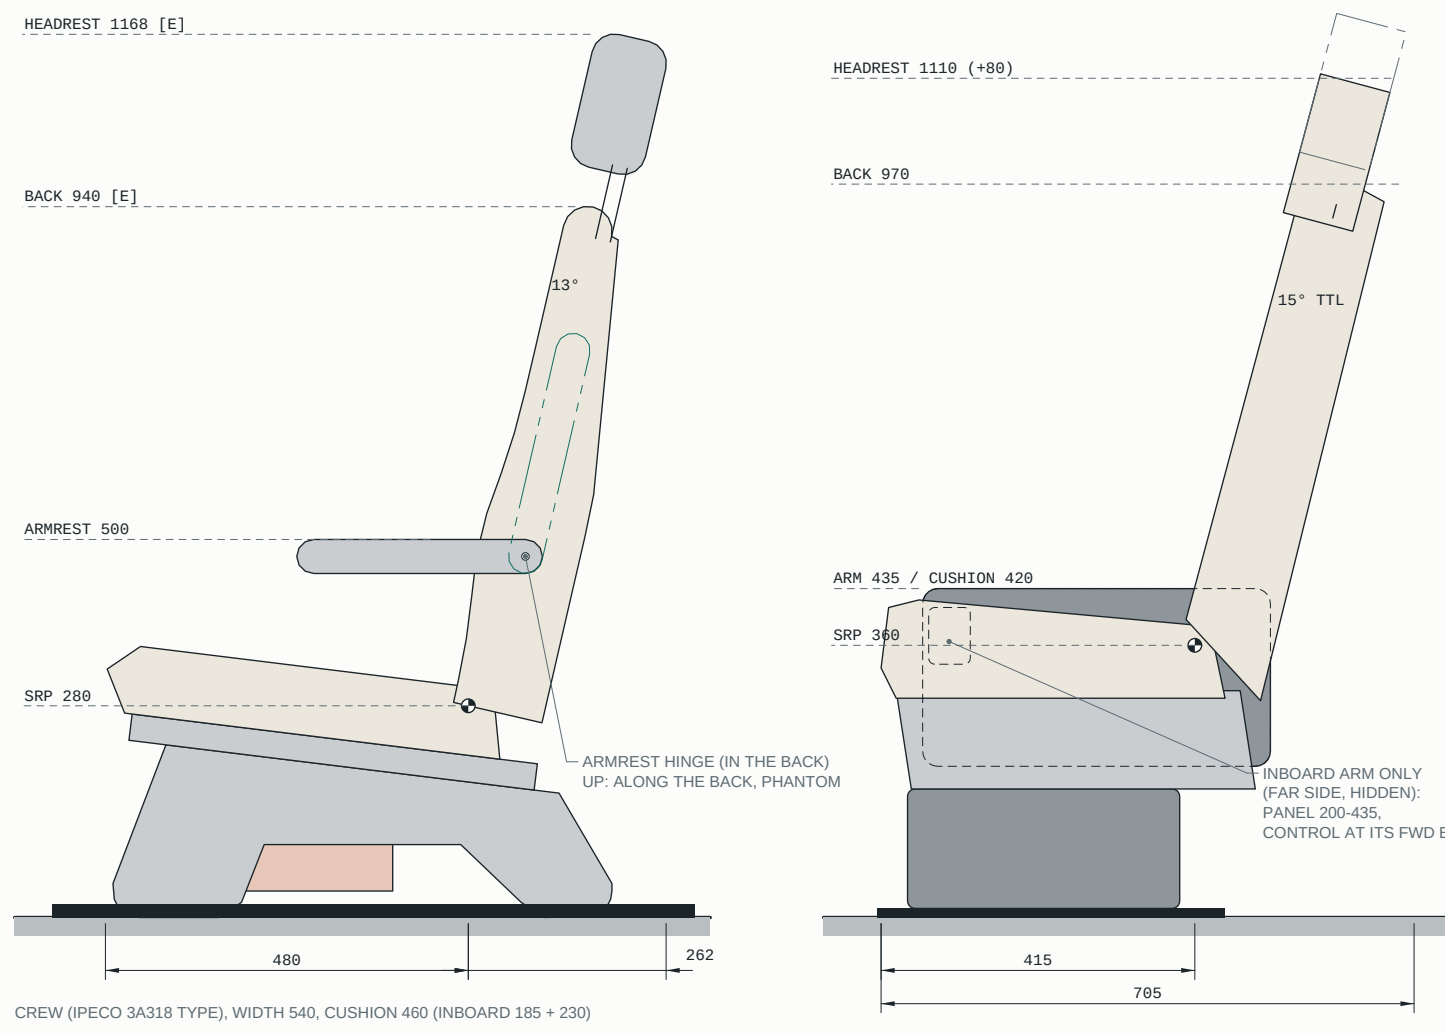

DETAIL E - SEATS
CREW (NEUTRAL) / EXECUTIVE (UPRIGHT), SEEN FROM PORT - HEIGHTS ABOVE THE FLOOR - SCALE 1:10

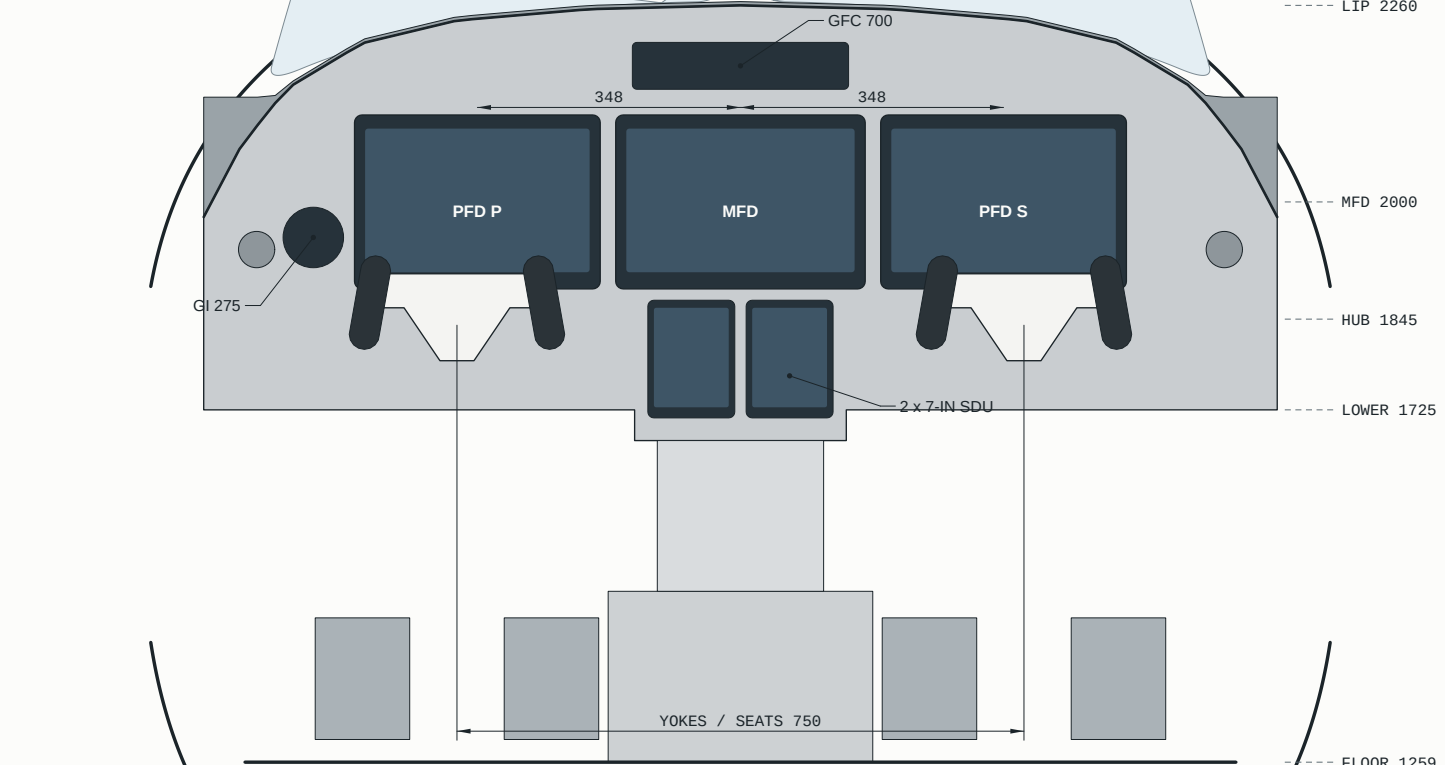

VIEW D - PANEL
LOOKING FORWARD (STBD RIGHT) AT STA 3500 - SCALE 1:10

RECONSTRUCTION FROM PUBLISHED DATA - NOT FOR CONSTRUCTION

RECONSTRUCTION FROM PUBLISHED DATA - NOT FOR CONSTRUCTION


RECONSTRUCTION FROM PUBLISHED DATA - NOT FOR CONSTRUCTION

RECONSTRUCTION FROM PUBLISHED DATA - NOT FOR CONSTRUCTION

RECONSTRUCTION FROM PUBLISHED DATA - NOT FOR CONSTRUCTION

SEAT MAP - EX-GS-2 (STA / BL mm)									
SEAT	FACING	BL	CUSH. FRONT	OCCUP. (POH)	SRP STA	BACK REAR	RECLINE	WINDOW	
P110T	FWD	-375	3720	4071	4200	4402	-	-	-
CO-PILOT	FWD	+375	3720	4071	4200	4402	-	-	-
PAX 1	AFT	-400	6242	5999	5827	5537	45°	P1 - 294	-
PAX 2	AFT	+400	6242	5999	5827	5537	42°	EX +386	-
PAX 3	FWD	-400	6776	7011	7191	7481	33°	P3 - 31	-
PAX 4	FWD	+400	6776	7011	7191	7481	45°	S2 - 31	-
PAX 5	FWD	-400	7945	8108	8360	8650	45°	CD - 222	-
PAX 6	FWD	+400	8250	8485	8695	8955	38°	S4 +9	-

Occupant = POH NCX Report (2006 WAB arm datum = model datum) Crew: centre notch, 170. Recline: reached, raised headrest (limit on L68). Window: nearest, offset.

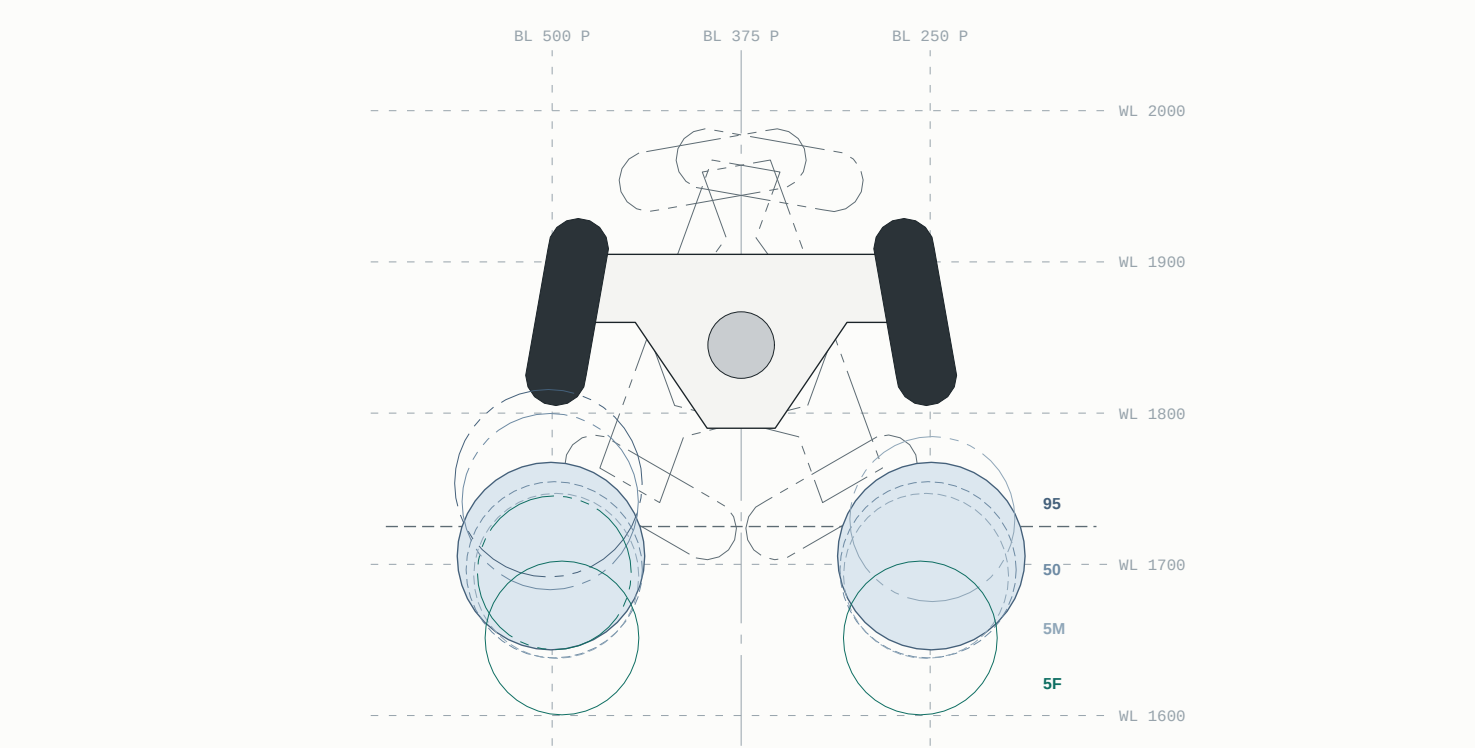

DETAIL F - YOKE SWEEP vs KNEES
LEFT SEAT, LOOKING FORWARD AT THE KNEES (STA 3653) - SCALE 1:5

RECONSTRUCTION FROM PUBLISHED DATA - NOT FOR CONSTRUCTION

RECONSTRUCTION FROM PUBLISHED DATA - NOT FOR CONSTRUCTION

